
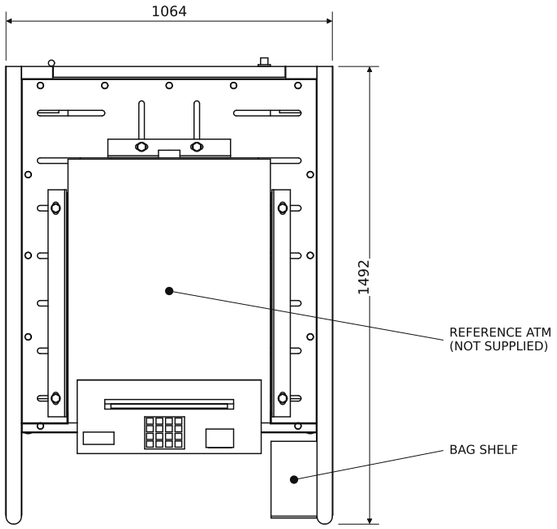


PLAN - SECTION A-A AT +1200 FFL

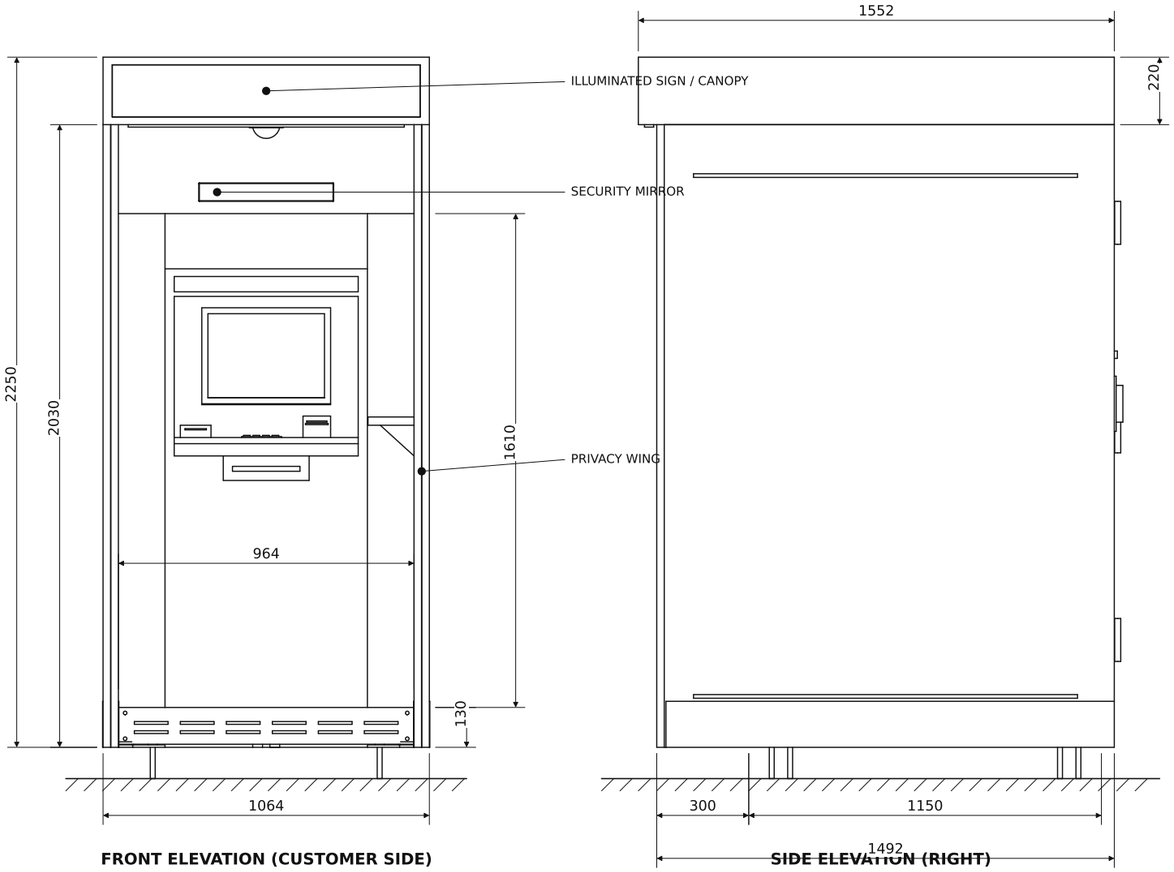

FRONT ELEVATION (CUSTOMER SIDE)

SIDE ELEVATION (RIGHT)

ISOMETRIC




GENERAL NOTES


1. Universal stand for floor-standing lobby ATMs: W 480-780, D 550-1000, H <= 1600 mm, mass <= 1000 kg (static).
2. Reference ATM shown for fit only - supplied by bank / OEM.
3. Floor: level concrete C25/30 min. 150 thk. Anchor with 8x M16 chemical anchors (125 embed.) after levelling +/-25 mm.
4. Interface heights per EN 1090-2 fabrication; customer zone kept clear 964 mm between wings. Check local accessibility code.
5. Finish: frame RAL 7016, wings RAL 9016, canopy brand colour.

PROJECT **UNIVERSAL ATM STAND - UATM-1000**	UNITS / TOLERANCE mm - ISO 2768-mK
TITLE **GENERAL ARRANGEMENT - KIOSK**	
DRAWING No. **UATM-1000-GA**	PROJECTION THIRD ANGLE


SCALE (A3)	DRAWN / DATE	REV	SHEET
1:20	CAD-gen 2026-10-26	**A**	**1 / 7**

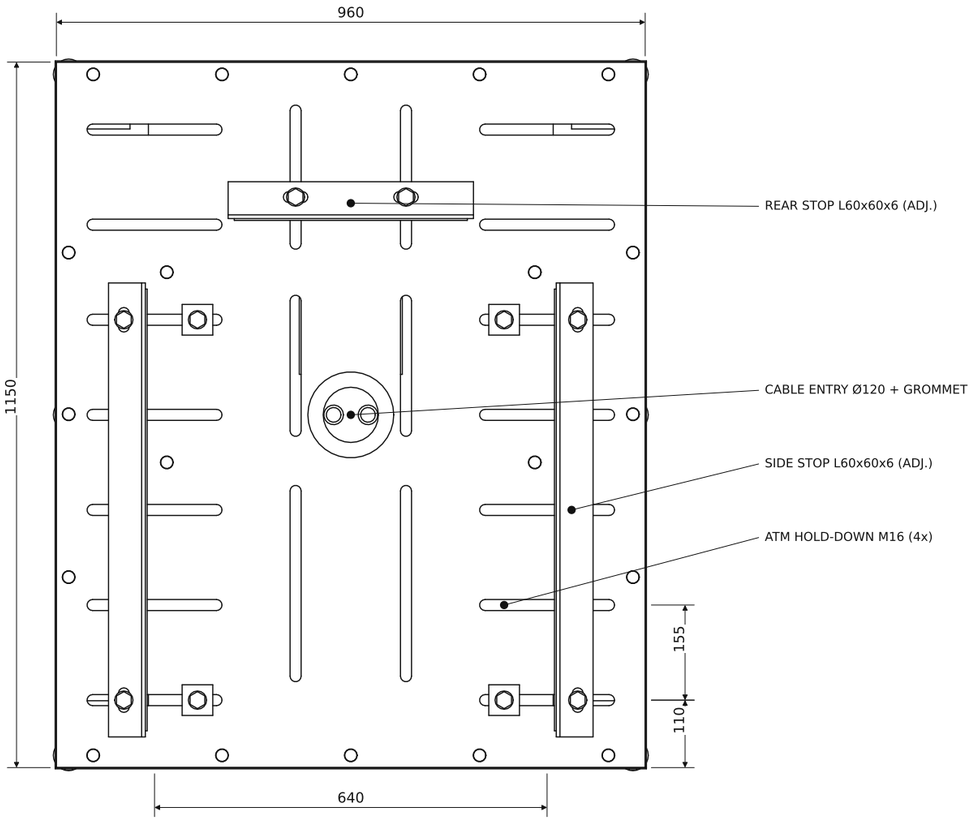

PLAN (DECK & CLAMP KIT)

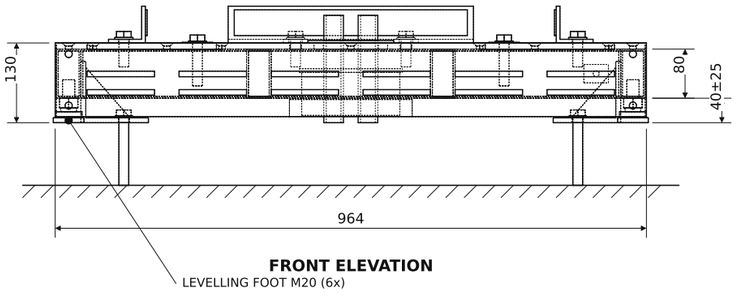


FRONT ELEVATION

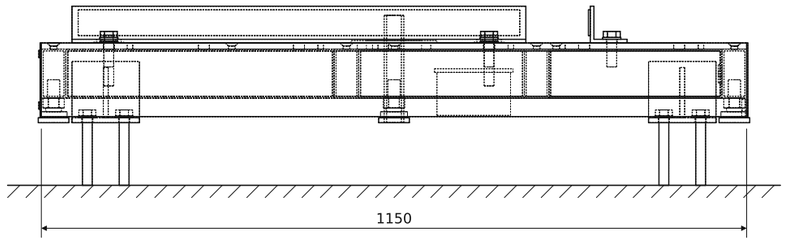

SIDE ELEVATION


ISOMETRIC

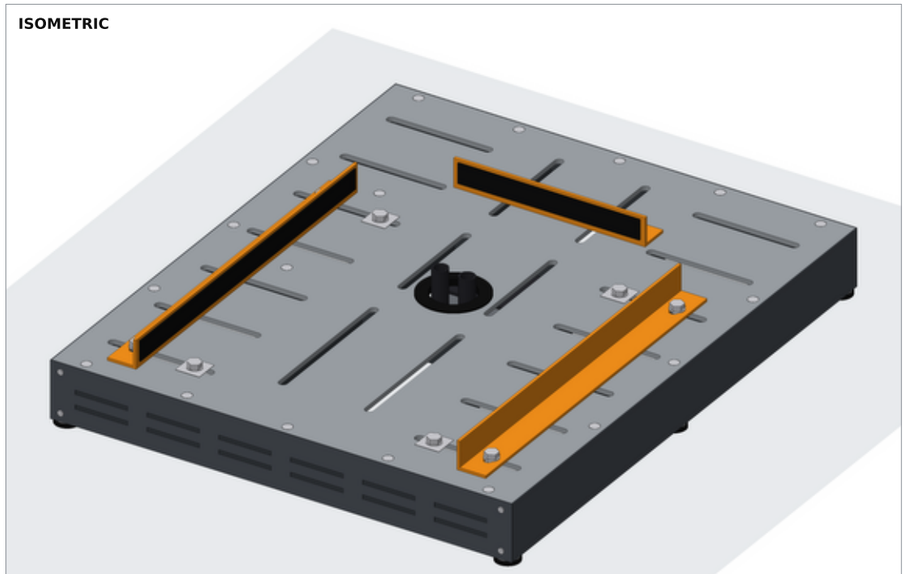

PLINTH NOTES

1. Deck: 10 mm S355 laser cut, M10 CSK to rivnuts in frame.
2. Universal slots 18 wide: 14x lateral (X), 6x longitudinal (Y).
3. Side/rear stops clamp with M16 T-bolts; set 5 mm clear of ATM with 3 mm EPDM strip, then torque 120 Nm.
4. ATM hold-down: M16 8.8 through ATM base, 50x50x6 clamp plate under deck. Torque per ATM OEM (typ. 140 Nm).
5. Level with 6x M20 feet (±25), then fix 8x M16 anchors.
6. Front service panel removable for under-deck access.
7. Design load 1000 kg static + 2 kN horizontal at 1.2 m.


PROJECT: **UNIVERSAL ATM STAND - UATM-1000**			UNITS / TOLERANCE: mm - ISO 2768-mK
TITLE: **PLINTH KIT ASSEMBLY**			
DRAWING No.: **UATM-1100**			PROJECTION: THIRD ANGLE
SCALE (A3): **1:10**	DRAWN / DATE: CAD-gen 2026-10-26	REV: **A**	SHEET: **2 / 7**

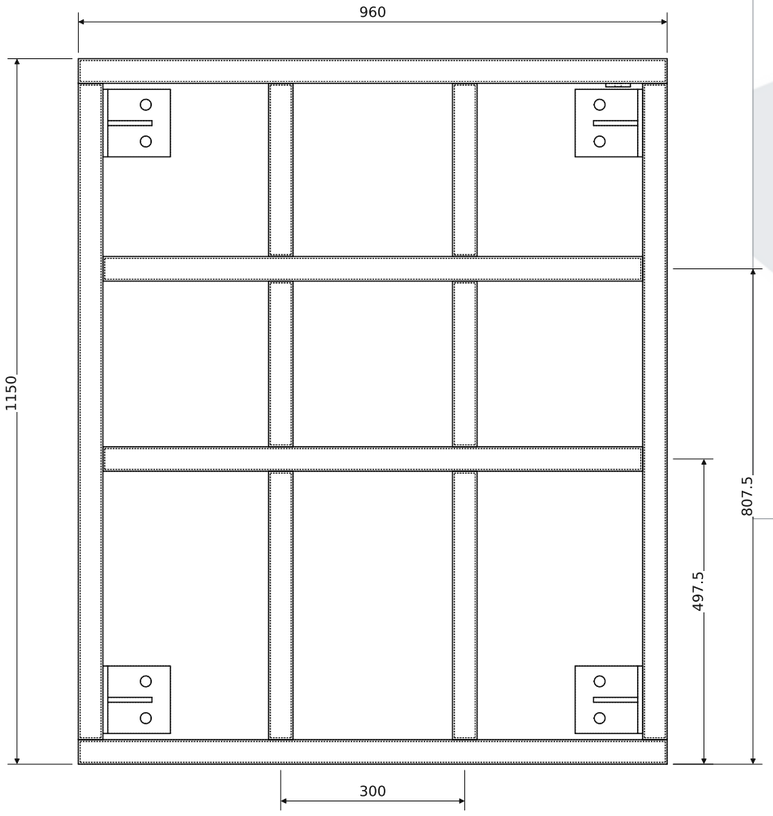

PLAN




FRONT ELEVATION

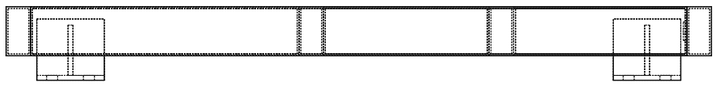

SIDE ELEVATION

ISOMETRIC (FROM REAR)

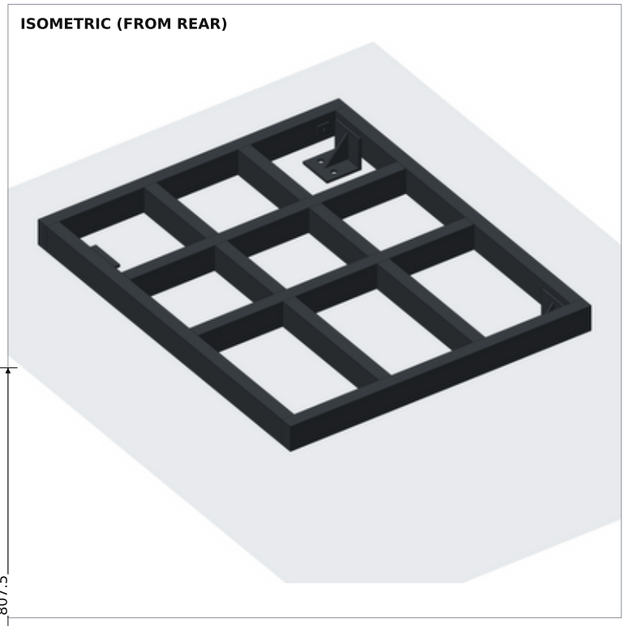


CUT LIST (S355J2H EN 10219)

Mk	Section	Member	Qty	L mm	kg/ea	kg
F1	RHS 80x40x3	Side Rail	2	1070	5.9	11.7
F2	RHS 80x40x3	Front Rail	2	960	5.3	10.5
F3	RHS 80x40x3	Cross Member	2	880	4.8	9.7
F4	RHS 80x40x3	Bearer	2	438	2.5	4.9
F5	RHS 80x40x3	Bearer	2	282	1.6	3.3
F6	RHS 80x40x3	Bearer	2	270	1.6	3.1
B1	PL 110x110x8 + upst.	Anchor bracket	4	-	-	-
L1	PL 40x30x6	Earth lug	1	-	-	-

WELDING & FINISH

1. All joints fillet weld a3 all round, MIG (135), EN ISO 5817-C.
2. Butt-jointed RHS, ends closed by adjoining member; open ends of front/rear rails seal-welded with 3 mm cap plates.
3. Frame square within 2 mm across diagonals; top face flat within 1.5 mm over full length (deck seating).
4. M20 weld nuts at 6x foot positions inside side rails.
5. M10 rivnuts (20x) in top face for deck fixing - drill Ø13.
6. Hot-dip galvanise ISO 1461 after welding, vent holes Ø10 at member ends (not shown), then powder coat RAL 7016.

PROJECT **UNIVERSAL ATM STAND - UATM-1000**			UNITS / TOLERANCE mm - ISO 2768-mK
TITLE **BASE FRAME WELDMENT**			
DRAWING No. **UATM-1110**			PROJECTION THIRD ANGLE
SCALE (A3) **1:10**	DRAWN / DATE CAD-gen 2026-10-26	REV **A**	SHEET **3 / 7**

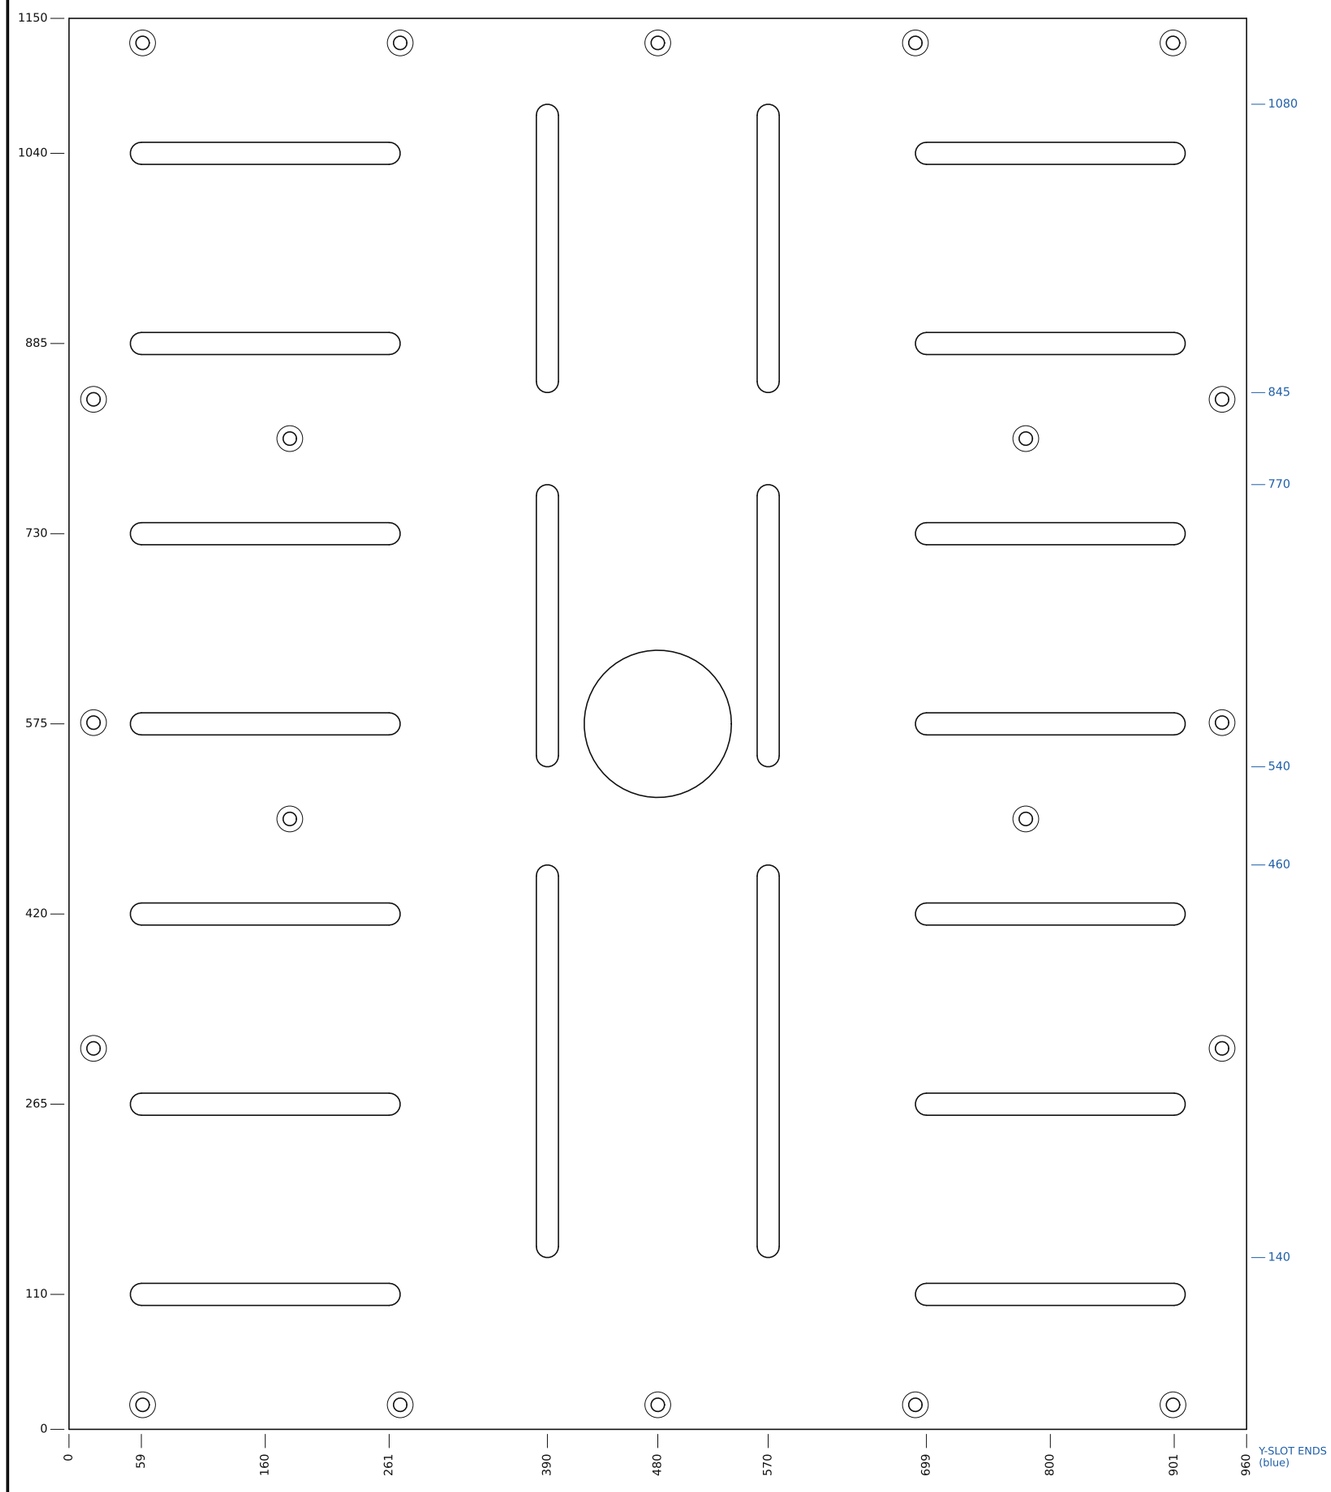


PLAN - DECK PLATE 10 mm (DATUM A/B AT FRONT-LEFT CORNER)

FEATURE TABLE

Ref	Feature	Qty	Purpose
S1	Slot 18 x 220 (lateral X)	14	M16 T-bolt / ATM anchor
S2	Slot 18 x var. (longit. Y)	6	Rear stop / ATM anchor
H1	Ø120 through	1	Cable entry + grommet
H2	Ø11 csk 90° x Ø21	20	M10 CSK to frame rivnut

PLATE NOTES

1. Material S355J2+N EN 10025-2, 10 mm, flatness 2 mm/m.
2. Laser / plasma cut to DXF 'Deck_Plate_10mm_S355.dxf'.
3. Slot pattern: X-slots centred +/-320, rows at 110 + n x 155 (n=0..6).
4. Y-slots on X = +/-90 between cross members.
5. Remove all burrs, break edges 0.5 x 45°.
6. Hot-dip galvanise ISO 1461 (85 µm), no paint on top face under ATM footprint (earth continuity).
7. Countersinks 90° to suit DIN 7991 M10 (flush +0 / -0.5).
8. Engrave 'UATM-1120 / FRONT' on top face front-left.
9. Ordinate dimensions from datum A (left edge) & B (front edge). Slot ordinates are to slot centres / arc centres.

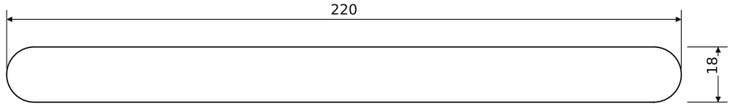


DETAIL C - SLOT S1 (1:2)

PROJECT **UNIVERSAL ATM STAND - UATM-1000**			UNITS / TOLERANCE mm - ISO 2768-mK
TITLE **UNIVERSAL DECK PLATE**			
DRAWING No. **UATM-1120**			PROJECTION THIRD ANGLE
SCALE (A3) **1:5**	DRAWN / DATE CAD-gen 2026-10-26	REV **A**	SHEET **4 / 7**

ADJUSTMENT RANGE

Item	Range (mm)	Method
Cabinet width	480 - 780	Side stops slide in X-slots
Cabinet depth	550 - 1000	Rear stop in Y-slots (+spacer)
Cabinet height	<= 1600	Below ceiling plate +1740
Fascia setback	0 - 60	Slot rows / spacer under stops
Mass	<= 1000 kg	4x M16 hold-down + 6 feet
Anchor pattern	any 4-bolt	Lands on slots; else drill 10 mm
Floor levelling	+/- 25	6x M20 swivel feet
Trim width	92 - 242	Telescopic stainless side trims

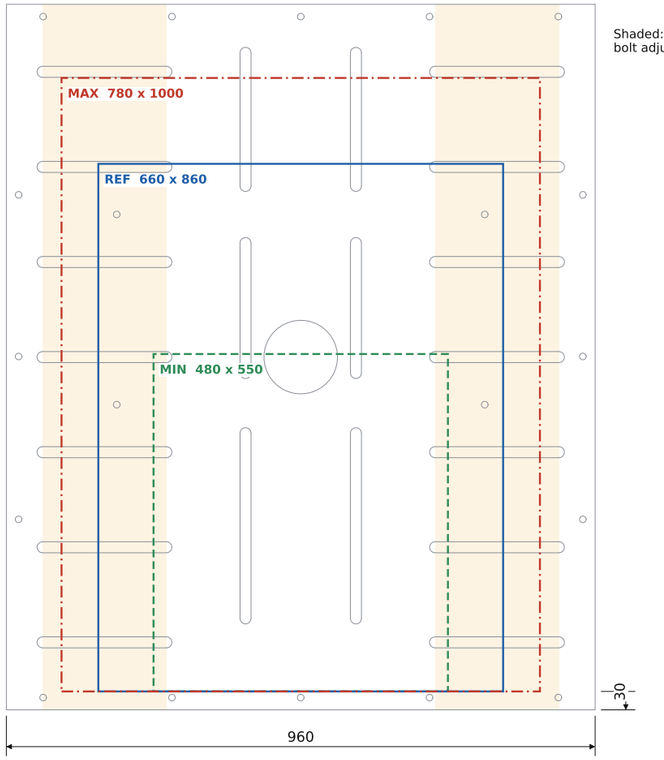

Shaded: side-stop / anchor bolt adjustment zone


ATM FOOTPRINT ENVELOPE ON DECK (PLAN)

ACCESSIBILITY

Reach limits shown per ADA 2010 §308 / EN 17210 guidance. Deck height 130 keeps operable parts of most lobby ATMs <= 1220. For tall cabinets reduce foot_h / deck height (parametric) - check OEM data. Clear floor space 760x1220 in front of fascia must be kept free of obstacles.

SIDE ELEVATION - REACH ZONES (1:20)

PROJECT: **UNIVERSAL ATM STAND - UATM-1000**			UNITS / TOLERANCE: mm - ISO 2768-mK
TITLE: **UNIVERSAL FIT & ACCESSIBILITY**			
DRAWING No.: **UATM-1000-UF**			PROJECTION: THIRD ANGLE
SCALE (A3): **1:10 / 1:20**	DRAWN / DATE: CAD-gen 2026-10-26	REV: **A**	SHEET: **5 / 7**

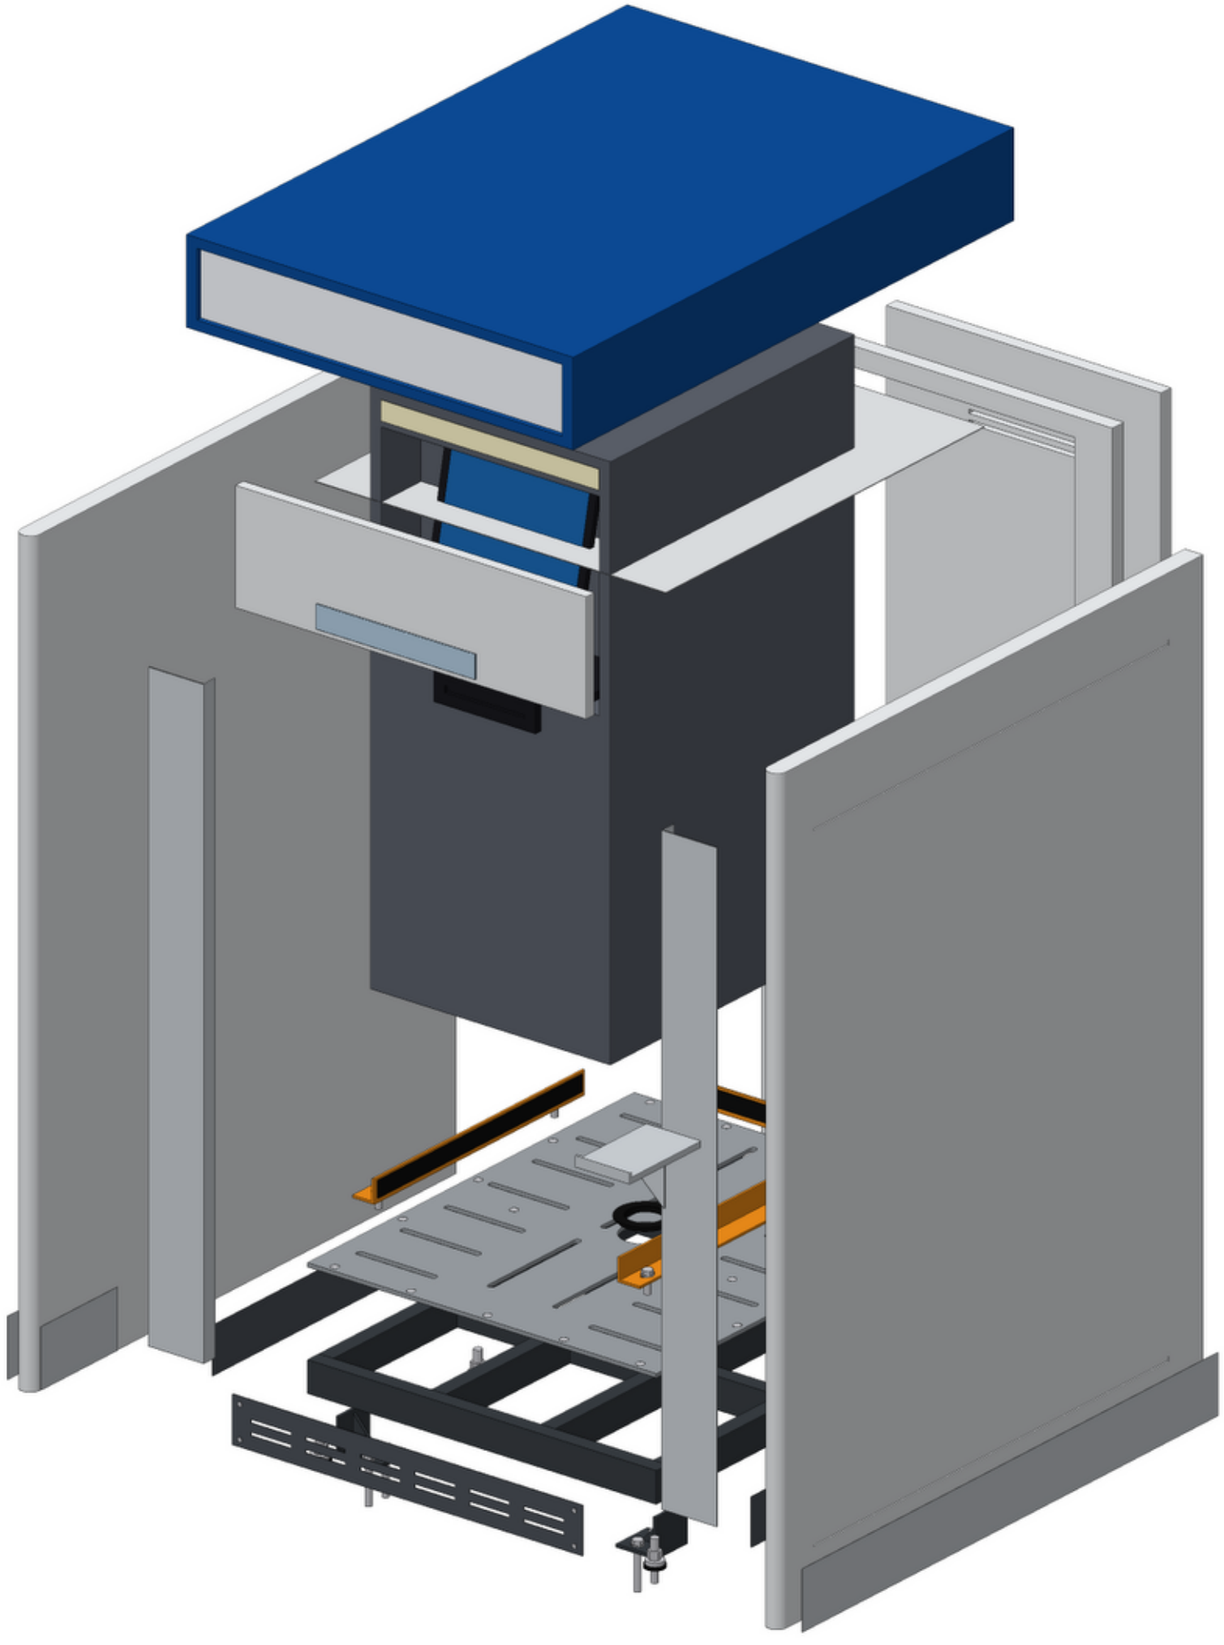

ASSEMBLY SEQUENCE

1. Mark out footprint; check floor flatness (<= 5 mm / 2 m).
2. Place base frame weldment; fit 6x M20 levelling feet.
3. Level frame (spirit level on top face, <= 1 mm / m).
4. Drill & set 8x M16 chemical anchors through brackets; cure per resin datasheet, torque 80 Nm.
5. Route power & data conduits; mount junction box.
6. Fit deck plate: 20x M10 CSK into rivnuts, 45 Nm.
7. Fit cable grommet; pre-set side & rear stops loosely.
8. Fit side, rear & front skirts (front = service panel).
9. Erect privacy wings; bolt to frame & floor (M10).
10. Fit rear wall + service door; check door swing & locks.
11. Fit canopy, sign face, LED + CCTV; wire to JB.
12. Lift ATM onto deck (pallet truck / gantry), push against rear stop, clamp side stops at 5 mm.
13. Fit 4x M16 hold-downs through ATM base; torque.
14. Fit telescopic side trims & front header panel.
15. Earth bond: frame lug -> ATM -> JB PE (< 0.1 ohm).
16. Commission: lighting, CCTV, mirror, locks, signage.

TOOLS & TORQUES

M10 CSK deck screws ..... 45 Nm (8.8)
M16 stop T-bolts ..... 120 Nm
M16 anchors ..... 80 Nm (resin)
M20 foot lock nuts ..... 150 Nm
M6 security Torx ..... 8 Nm

PROJECT **UNIVERSAL ATM STAND - UATM-1000**			UNITS / TOLERANCE mm - ISO 2768-mK
TITLE **EXPLODED VIEW & ASSEMBLY SEQUENCE**			
DRAWING No. **UATM-1000-EX**			PROJECTION THIRD ANGLE
SCALE (A3) **NTS**	DRAWN / DATE CAD-gen 2026-10-26	REV **A**	SHEET **6 / 7**

#	Assembly	Description	Material	Qty	Unit kg	Total kg
1	Base frame	RHS 80x40x3 S355, welded, 960 mm	S355 steel	2	5.27	10.6
2	Base frame	RHS 80x40x3 S355, welded, 1070 mm	S355 steel	2	5.86	11.7
3	Base frame	RHS 80x40x3 S355, welded, 880 mm	S355 steel	2	4.84	9.7
4	Base frame	RHS 80x40x3 S355, welded, 438 mm	S355 steel	2	2.47	4.9
5	Base frame	RHS 80x40x3 S355, welded, 270 mm	S355 steel	2	1.57	3.1
6	Base frame	RHS 80x40x3 S355, welded, 282 mm	S355 steel	2	1.64	3.3
7	Base frame	Earth bonding lug 40x30x6 c/w M10 stud	S355 steel	1	0.05	0.1
8	Levelling & anchoring	Levelling foot anti-slip pad Ø50	EPDM rubber	6	0.02	0.1
9	Levelling & anchoring	Levelling foot M20x60, swivel base, lock nut, 1500 kg SWL	Zinc-plated steel 8.8	6	0.32	1.9
10	Levelling & anchoring	Floor anchor bracket 110x110x8 + gusset, welded to side rail	S355 steel	4	1.55	6.2
11	Levelling & anchoring	Chemical anchor M16x160 A4 c/w nut & washer (125 embed.)	Zinc-plated steel 8.8	8	0.23	1.8
12	Deck & clamp kit	Universal deck plate 960x1150x10, laser cut slot pattern, HDG	S355 steel	1	79.08	79.1
13	Deck & clamp kit	M10x30 countersunk screw DIN 7991 + rivnut (set of 20)	Zinc-plated steel 8.8	1	0.14	0.1
14	Deck & clamp kit	Cable entry grommet Ø120 / Ø90 brush insert	EPDM rubber	1	0.10	0.1
15	Deck & clamp kit	Adjustable side stop L60x60x6, slotted, L=740	S355 steel	2	3.91	7.8
16	Deck & clamp kit	EPDM anti-vibration strip 3 mm	EPDM rubber	3	0.09	0.3
17	Deck & clamp kit	T-head bolt M16x45 + washer + nyloc (slot clamp)	Zinc-plated steel 8.8	6	0.13	0.8
18	Deck & clamp kit	Adjustable rear stop L60x60x6, L=400	S355 steel	1	2.09	2.1
19	Deck & clamp kit	ATM hold-down M16x70 8.8 + 50x50x6 under-deck clamp plate	Zinc-plated steel 8.8	4	0.18	0.7
20	Skirting	Front kick / service panel 2 mm, louvred, 4x M6 security Torx	Galv. steel	1	1.63	1.6
21	Skirting	M6 pin-Torx security screw (set of 4)	Stainless 304	1	0.01	0.0
22	Skirting	Side skirt 2 mm	Galv. steel	2	2.17	4.3
23	Skirting	Rear skirt 2 mm c/w 200x28 cable mouse-hole	Galv. steel	1	1.73	1.7
24	Skirting	Brush strip 200 mm for surface-run cable entry	Nylon	1	0.04	0.0
25	Services	Flexible conduit Ø32 (power), floor to ATM	Nylon	1	0.07	0.1
26	Services	Flexible conduit Ø32 (data), floor to ATM	Nylon	1	0.07	0.1
27	Services	IP65 junction box 160x120x75 c/w 16 A fused spur + RCBO	ABS / PA	1	1.48	1.5
28	Services	Junction box lid	ABS / PA	1	0.14	0.1
29	Privacy wings	Privacy wing 50 mm, 1.5 mm Zintec skins on 40x40 frame, powder coat RAL 9016	Galv. steel	2	62.67	125.3
30	Privacy wings	Kick plate 1.5 mm brushed stainless	Stainless 304	4	1.56	6.2
31	Privacy wings	Customer bag shelf 250x150 stainless	Stainless 304	1	4.59	4.6
32	Privacy wings	Shelf gusset 6 mm	Stainless 304	1	0.26	0.3
33	Canopy	Canopy / topper 2 mm aluminium folded box, powder coat brand colour	Aluminium 6063	1	25.84	25.8
34	Canopy	Illuminated sign face 5 mm opal acrylic (graphics by others)	Opal acrylic	1	1.02	1.0
35	Canopy	LED linear downlight 900 mm, 24 V, 4000 K, 500 lux at keypad	Aluminium 6063	1	0.58	0.6
36	Canopy	Vandal-proof IP dome camera (by bank)	Polycarbonate	1	0.27	0.3
37	Canopy	LED driver 24 V 60 W + photocell/timer	Aluminium 6063	1	1.94	1.9
38	Header & trims	Front header panel 2 mm, removable	Galv. steel	1	4.94	4.9
39	Header & trims	Rear-view security mirror 440x60, acrylic	Glass mirror	1	0.33	0.3
40	Header & trims	Telescopic side trim 3 mm stainless (cut to ATM width, here 152 mm)	Stainless 304	2	7.30	14.6
41	Header & trims	Internal ceiling / anti-intrusion plate 2 mm	Galv. steel	1	16.98	17.0
42	Rear wall & door	Rear service wall 40 mm composite, door frame	Galv. steel	1	14.50	14.5
43	Rear wall & door	Service door 760x1900, 2 mm skins, 3-point locking	Galv. steel	1	31.18	31.2
44	Rear wall & door	Heavy-duty concealed-pin hinge (x3)	Stainless 304	1	1.06	1.1
45	Rear wall & door	Swing handle, 3-point rod espagnolette	Stainless 304	1	0.85	0.8
46	Rear wall & door	High-security cylinder lock (keyed alike)	Stainless 304	1	0.04	0.0

PLINTH KIT: 154 kg **COMPLETE (EXCL. ATM): 404 kg**

PROJECT **UNIVERSAL ATM STAND - UATM-1000**			UNITS / TOLERANCE mm - ISO 2768-mK
TITLE **BILL OF MATERIALS**			
DRAWING No. **UATM-1000-BOM**			PROJECTION THIRD ANGLE
SCALE (A3) -	DRAWN / DATE CAD-gen 2026-10-26	REV **A**	SHEET **7 / 7**